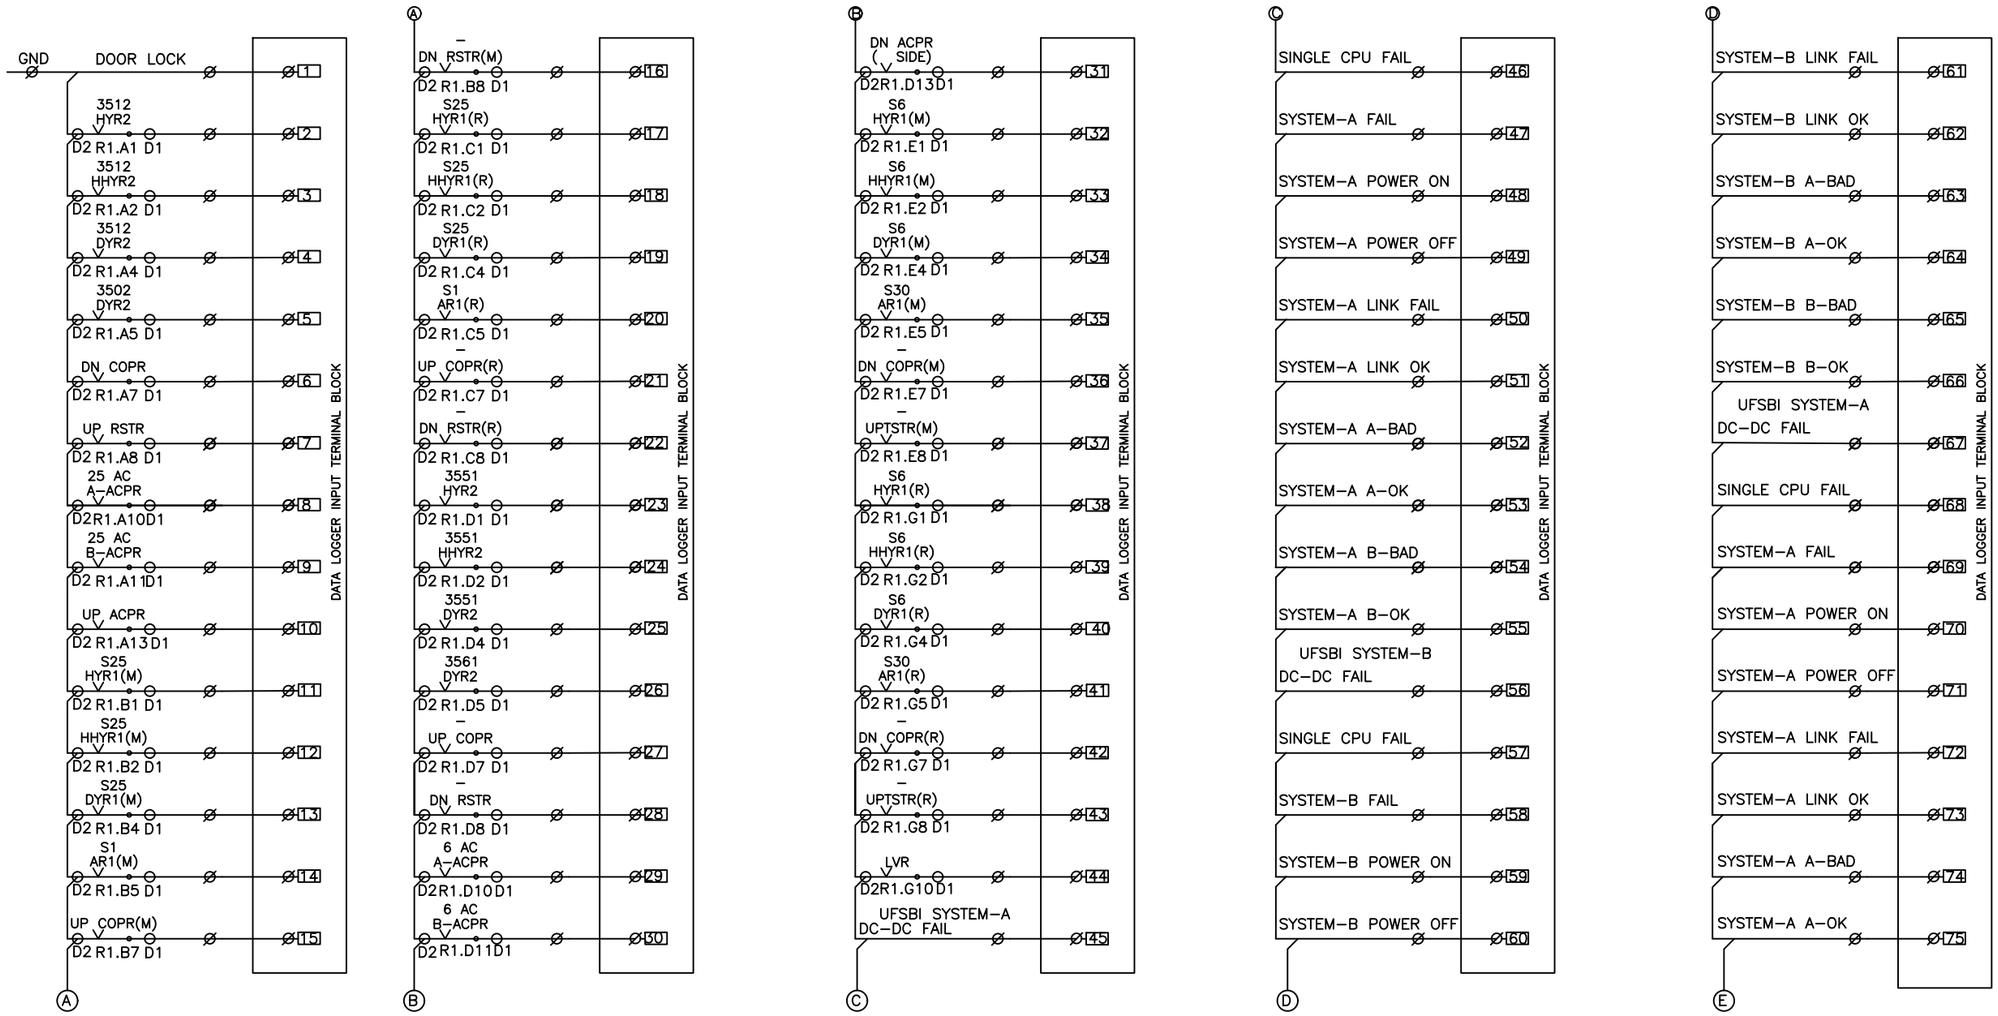
DATA LOGGER


GND
DOOR LOCK
3512 HYR2 D2 R1.A1 D1
3512 HHYR2 D2 R1.A2 D1
3512 DYR2 D2 R1.A4 D1
3502 DYR2 D2 R1.A5 D1
DN COPR D2 R1.A7 D1
UP RSTR D2 R1.A8 D1
25 AC A-ACPR D2R1.A10D1
25 AC B-ACPR D2 R1.A11D1
UP ACPR D2 R1.A13 D1
S25 HYR1(M) D2 R1.B1 D1
S25 HHYR1(M) D2 R1.B2 D1
S25 DYR1(M) D2 R1.B4 D1
S1 AR1(M) D2 R1.B5 D1
UP COPR(M) D2 R1.B7 D1
DN RSTR(M) D2 R1.B8 D1
S25 HYR1(R) D2 R1.C1 D1
S25 HHYR1(R) D2 R1.C2 D1
S25 DYR1(R) D2 R1.C4 D1
S1 AR1(R) D2 R1.C5 D1
UP COPR(R) D2 R1.C7 D1
DN RSTR(R) D2 R1.C8 D1
3551 HYR2 D2 R1.D1 D1
3551 HHYR2 D2 R1.D2 D1
3551 DYR2 D2 R1.D4 D1
3561 DYR2 D2 R1.D5 D1
UP COPR D2 R1.D7 D1
DN RSTR D2 R1.D8 D1
6 AC A-ACPR D2R1.D10D1
6 AC B-ACPR D2R1.D11D1
DN ACPR (SIDE) D2R1.D13D1
S6 HYR1(M) D2 R1.E1 D1
S6 HHYR1(M) D2 R1.E2 D1
S6 DYR1(M) D2 R1.E4 D1
S30 AR1(M) D2 R1.E5 D1
DN COPR(M) D2 R1.E7 D1
UPTSTR(M) D2 R1.E8 D1
S6 HYR1(R) D2 R1.G1 D1
S6 HHYR1(R) D2 R1.G2 D1
S6 DYR1(R) D2 R1.G4 D1
S30 AR1(R) D2 R1.G5 D1
DN COPR(R) D2 R1.G7 D1
UPTSTR(R) D2 R1.G8 D1
LVR D2R1.G10D1
UFSBI SYSTEM-A DC-DC FAIL
SINGLE CPU FAIL
SYSTEM-A FAIL
SYSTEM-A POWER ON
SYSTEM-A POWER OFF
SYSTEM-A LINK FAIL
SYSTEM-A LINK OK
SYSTEM-A A-BAD
SYSTEM-A A-OK
SYSTEM-A B-BAD
SYSTEM-A B-OK
UFSBI SYSTEM-B DC-DC FAIL
SINGLE CPU FAIL
SYSTEM-B FAIL
SYSTEM-B POWER ON
SYSTEM-B POWER OFF
SYSTEM-B LINK FAIL
SYSTEM-B LINK OK
SYSTEM-B A-BAD
SYSTEM-B A-OK
SYSTEM-B B-BAD
SYSTEM-B B-OK
UFSBI SYSTEM-A DC-DC FAIL
SINGLE CPU FAIL
SYSTEM-A FAIL
SYSTEM-A POWER ON
SYSTEM-A POWER OFF
SYSTEM-A LINK FAIL
SYSTEM-A LINK OK
SYSTEM-A A-BAD
SYSTEM-A A-OK
DATA LOGGER INPUT TERMINAL BLOCK
A
B
C
D
E